งานระบบปรับอากาศและน้ำเย็น — อาคารอ้างอิง 8 ชั้น (CPMS V7.9)

CPMS REFERENCE BUILDING V7.9 · CHILLER PLANT (MAX 6 PER TYPE) · AIR SIDE · MODEL-GENERATED DRAWING SET

รายการแบบ / DRAWING LIST

M-000	ปก รายการแบบ สัญลักษณ์ หมายเหตุทั่วไป
M-101	แปลนชั้น 1 ทั้งอาคาร 1:200
M-102	แปลนห้องเครื่องทำน้ำเย็น 1:100
M-103	แปลนดาดฟ้า cooling tower 1:100
M-104	แปลนชั้นทั่วไป 2-8 air side 1:200
M-201	รูปตัดอาคาร 1:200
M-501	แผนผังระบบท่อ CHW / CDW (6 slot)
M-502	แผนผัง riser น้ำเย็นไป AHU
M-601	ตารางอุปกรณ์

สัญลักษณ์ / SYMBOLS

- BFV — Butterfly valve, lug type, PN16
- MBFV — Motorized butterfly valve (on/off, 24 Vac)
- MCV — Motorized control valve (modulating 0-10 V, position feedback)
- CHECK — Check valve, silent / dual plate
- STRAINER — Y-strainer, 20 mesh
- FLEX — Flexible connector, EPDM double sphere
- RED_E — Eccentric reducer
- RED_C — Concentric increaser
- CAP — End cap / blind flange (header stub)
- DRAIN — Drain valve 1-1/2" c/w hose cap
- PG — Pressure gauge 0-10 bar c/w cock
- TT — Temperature sensor 10k thermistor in well + thermometer
- FS — Paddle flow switch
- FM — Electromagnetic flow meter
- PT — Differential pressure transmitter 0-4 bar
- AAV — Automatic air vent 3/4" c/w isolating ball valve

เส้นท่อ / PIPE SERVICES

- CHS — Chilled water supply (หุ้มฉนวน)
- CHR — Chilled water return (หุ้มฉนวน)
- CDS — Condenser water supply
- CDR — Condenser water return

หมายเหตุทั่วไป / GENERAL NOTES

1. แบบชุดนี้สร้างอัตโนมัติจาก model79.py ชุดเดียวกับกราฟิก 3D และ BOQ — แก้ที่ทะเบียน/แบบจำลองแล้วสร้างใหม่ทั้งชุด
2. เป็นแบบอ้างอิงสำหรับ logic และกราฟิก ขนาดและตำแหน่งต้องออกแบบ/สำรวจยืนยันตามโครงการจริง
3. หน่วยวัดเป็นมิลลิเมตร ระดับอ้างอิงพื้นชั้น 1 ±0.000
4. ท่อน้ำเย็น/น้ำระบายความร้อน: ท่อเหล็กดำ ASTM A53 Sch.40 ข้อต่อเชื่อม/หน้าแปลน PN16
5. ท่อน้ำเย็นหุ้มฉนวนยางสังเคราะห์ 25 มม. คาดแถบสีและลูกศรทิศทางการไหลทุก 3 ม.
6. อุปกรณ์เส้นประ = slot ที่เตรียมพื้นที่/tee ไว้แต่ยังไม่ติดตั้ง (Installed = N ในทะเบียน)
7. การออกแบบอ้างอิงมาตรฐานระบบปรับอากาศ วสท. และ ASHRAE
8. วาล์ว M / C และเครื่องมือวัดเชื่อมกับ BMS ALT_CP_Ref_V7_9 ตาม Field IO register
9. ผู้รับจ้างต้องจัดทำ shop drawing ลงนามโดยวิศวกรผู้มีใบอนุญาตก่อนดำเนินการ

คำย่อ / ABBREVIATIONS

CH	เครื่องทำน้ำเย็น (Chiller)
CHP	ปั๊มน้ำเย็น
CDP	ปั๊มน้ำระบายความร้อน
CT	หอระบายความร้อน
CHS/CHR	น้ำเย็นจ่าย/กลับ
CDS/CDR	น้ำระบายความร้อนจ่าย/กลับ
BFV	วาล์วผีเสื้อ
MBFV	วาล์วผีเสื้อมอเตอร์
MCV	วาล์วควบคุมมอเตอร์
AAV	วาล์วระบายอากาศอัตโนมัติ
ET	ถังขยายตัว
DPB	ชุดบายพาสแรงดันต่าง
FFS	ระดับผิวพื้นสำเร็จ
FFL	ระดับพื้นหลังคา
NTS	ไม่ได้ย่อส่วน
BMS	ระบบควบคุมอาคาร

AETERLINK
AETERLINK (THAILAND) CO., LTD. · BMS / CPMS

PROJECT / โครงการ :
อาคารอ้างอิง 8 ชั้น (CPMS V7.9)
CPMS Reference Building V7.9
STATION :
ALT_CP_Ref_V7_9

OWNER / เจ้าของโครงการ :
[ระบุตามโครงการ]

BASIS / ที่มา :
Reference design for logic & graphics
Max. equipment 6 / type (register)
Site survey: NOT DONE (ต้องสำรวจ)

ENGINEERS / วิศวกรผู้ออกแบบ-ตรวจสอบ
วิศวกรเครื่องกล : .....
ใบอนุญาต ภก./สก. เลขที่ : .....
ลงนาม : ..... วันที่ : .....
วิศวกรไฟฟ้า : .....
ใบอนุญาต ภฟ./สฟ. เลขที่ : .....

REVISION / แก้ไข

A	08/10/2026	FOR REVIEW - generated from the V7.9 model

FOR REVIEW · ไม่ใช่แบบก่อสร้าง
NOT FOR CONSTRUCTION


DRAWING TITLE / ชื่อแบบ :
ปก รายการแบบ สัญลักษณ์ และหมายเหตุทั่วไป
COVER, DRAWING LIST, LEGEND & GENERAL NOTES

DRAWN : AETERLINK model generator
CHECKED : .....
APPROVED : .....
SCALE : NTS DATE : 08/10/2026

DRAWING NO. / เลขที่แบบ

M-000

หน่วยวัดเป็นมิลลิเมตร ระดับอ้างอิงพื้นชั้น 1 ±0.000

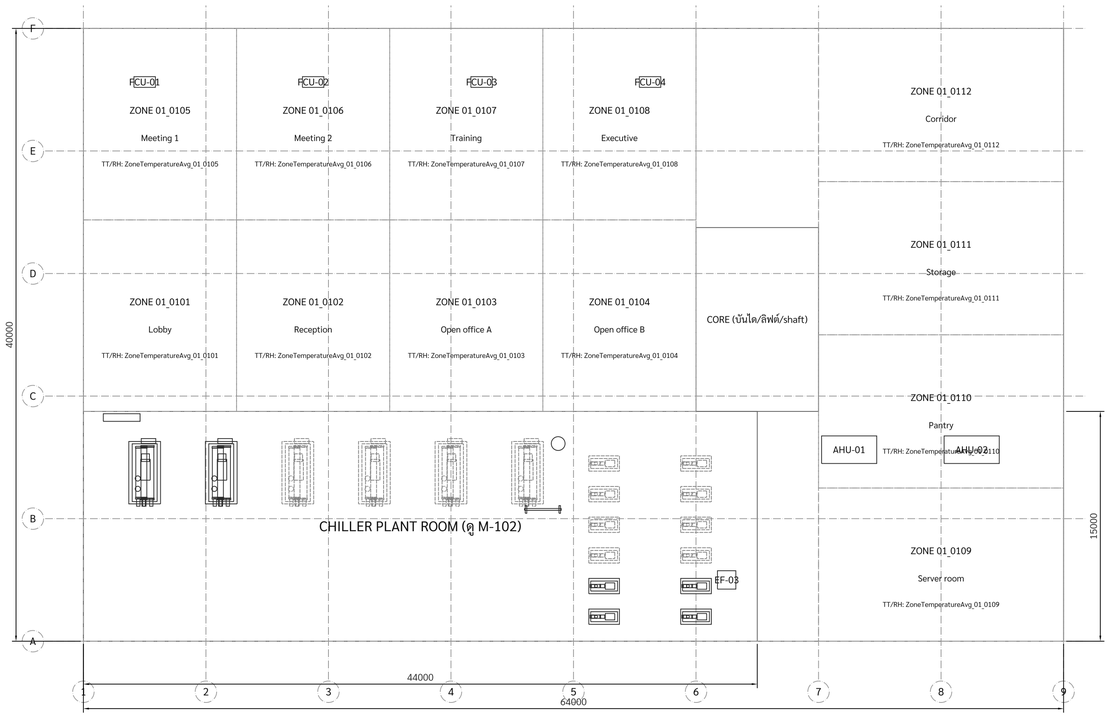

1 แปลนชั้น 1 / GROUND FLOOR PLAN

มาตราส่วน 1:200

หมายเหตุ / NOTES

1. ห้องเครื่องทำน้ำเย็น 44.0 x 15.0 ม. สูง 5.5 ม. ด้านทิศใต้-ตะวันตกของอาคาร
2. Zone 01_0101..0112 = จุด ZoneTemperatureAvg / ZoneHumidityAvg ใน station
3. AHU-01 / AHU-02 / FCU-01..04 = air side ชั้น 1 (V7.8)
4. ท่อ CHW ขึ้นอาคารผ่าน shaft ข้าง core (ดู M-104, M-502)

N

AETERLINK

AETERLINK (THAILAND) CO., LTD. · BMS / CPMS

PROJECT / โครงการ :
อาคารอ้างอิง 8 ชั้น (CPMS V7.9)
CPMS Reference Building V7.9
STATION :
ALT_CP_Ref_V7_9

OWNER / เจ้าของโครงการ :
[ระบุตามโครงการ]

BASIS / ที่มา :
Reference design for logic & graphics
Max. equipment 6 / type (register)
Site survey: NOT DONE (ต้องสำรวจ)

ENGINEERS / วิศวกรผู้ออกแบบ-ตรวจสอบ
วิศวกรเครื่องกล : .....
ใบอนุญาต ภก./สก. เลขที่ : .....
ลงนาม : ..... วันที่ : .....
วิศวกรไฟฟ้า : .....
ใบอนุญาต ภฟ./สฟ. เลขที่ : .....

REVISION / แก้ไข

A	08/10/2026	FOR REVIEW - generated from the V7.9 model

FOR REVIEW · ไม่ใช่แบบก่อสร้าง
NOT FOR CONSTRUCTION


DRAWING TITLE / ชื่อแบบ :
แปลนชั้น 1 ทั้งอาคาร (ห้องเครื่อง + พื้นที่ใช้งาน)
GROUND FLOOR PLAN - BUILDING

DRAWN : AETERLINK model generator
CHECKED : .....
APPROVED : .....
SCALE : 1:200 DATE : 08/10/2026

DRAWING NO. / เลขที่แบบ

M-101

หน่วยวัดเป็นมิลลิเมตร ระดับอ้างอิงพื้นชั้น 1 ±0.000

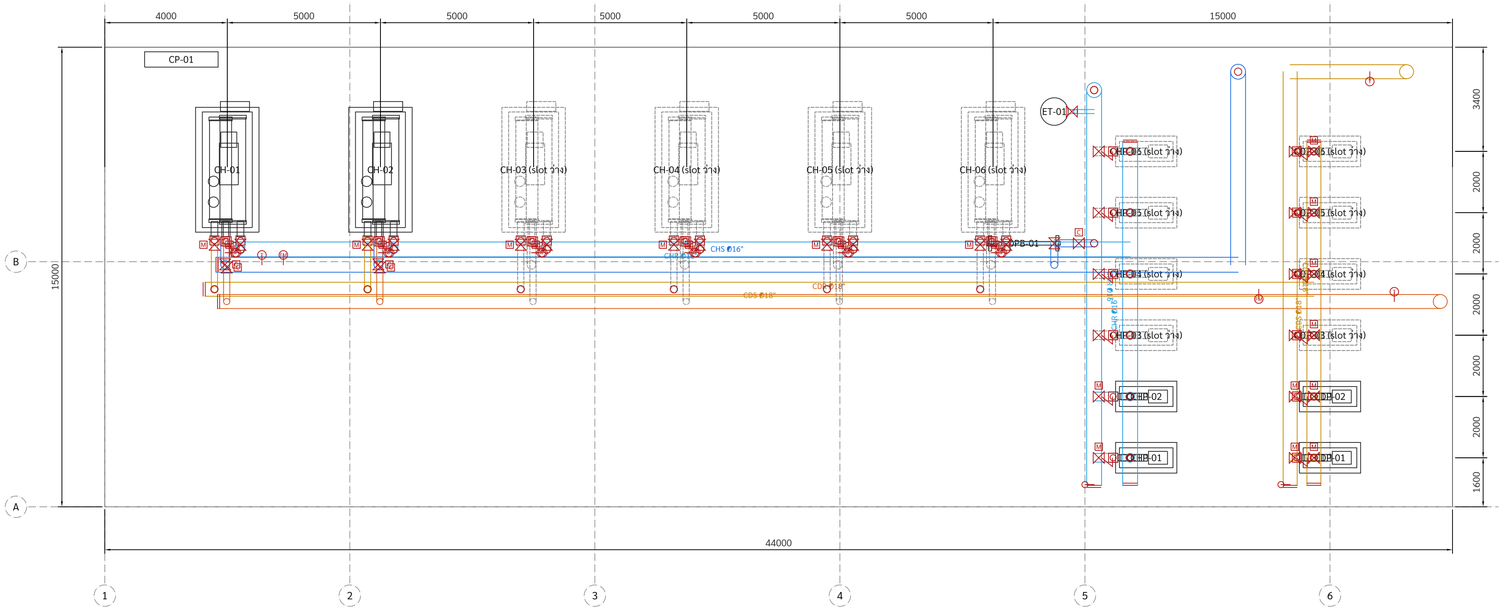

2 แปลนห้องเครื่อง / PLANT ROOM PLAN

มาตราส่วน 1:100

หมายเหตุ / NOTES

1. เส้นประ = slot ที่ยังไม่ติดตั้ง (CHxx/CHPxx/CDPxx/CTxx _Installed = ปิด) เผื่อพีนท์ ฐาน และ tee ไว้แล้ว
2. Header ทุกเส้นเป็นท่อตรง ปลาย cap + drain · riser ขึ้นอาคาร/ดาดฟ้าใน shaft
3. ระดับศูนย์ท่อ: ดูดปั๊ม +0.620 · CDW ไป condenser +1.800 · CHW ไป evaporator +2.600 · CHS +3.300 · CDR +4.200
4. Chiller ทุกเครื่องมี MBFV ฝั่งน้ำเย็น/น้ำระบายความร้อน + flow switch · ปั๊มมี check + MBFV ด้านจ่าย
5. ปั๊ม CHP / CDP แบบ headered: จำนวนเครื่องเดินตามจำนวน chiller ที่ต้องการน้ำ (v79_scale.py)

N

AETERLINK

AETERLINK (THAILAND) CO., LTD. · BMS / CPMS

PROJECT / โครงการ :
อาคารอ้างอิง 8 ชั้น (CPMS V7.9)
CPMS Reference Building V7.9
STATION :
ALT_CP_Ref_V7_9

OWNER / เจ้าของโครงการ :
[ระบุตามโครงการ]

BASIS / ที่มา :
Reference design for logic & graphics
Max. equipment 6 / type (register)
Site survey: NOT DONE (ต้องสำรวจ)

ENGINEERS / วิศวกรผู้ออกแบบ-ตรวจสอบ
วิศวกรเครื่องกล : .....
ใบอนุญาต ภก./สก. เลขที่ : .....
ลงนาม : ..... วันที่ : .....
วิศวกรไฟฟ้า : .....
ใบอนุญาต ภฟ./สฟ. เลขที่ : .....

REVISION / แก้ไข

A	08/10/2026	FOR REVIEW - generated from the V7.9 model

FOR REVIEW · ไม่ใช่แบบก่อสร้าง
NOT FOR CONSTRUCTION


DRAWING TITLE / ชื่อแบบ :
แปลนห้องเครื่องทำน้ำเย็น (สูงสุด 6 ชุดต่อชนิด)
CHILLER PLANT ROOM PLAN

DRAWN : AETERLINK model generator
CHECKED : .....
APPROVED : .....
SCALE : 1:100 DATE : 08/10/2026

DRAWING NO. / เลขที่แบบ

M-102

หน่วยวัดเป็นมิลลิเมตร ระดับอ้างอิงพื้นชั้น 1 ±0.000

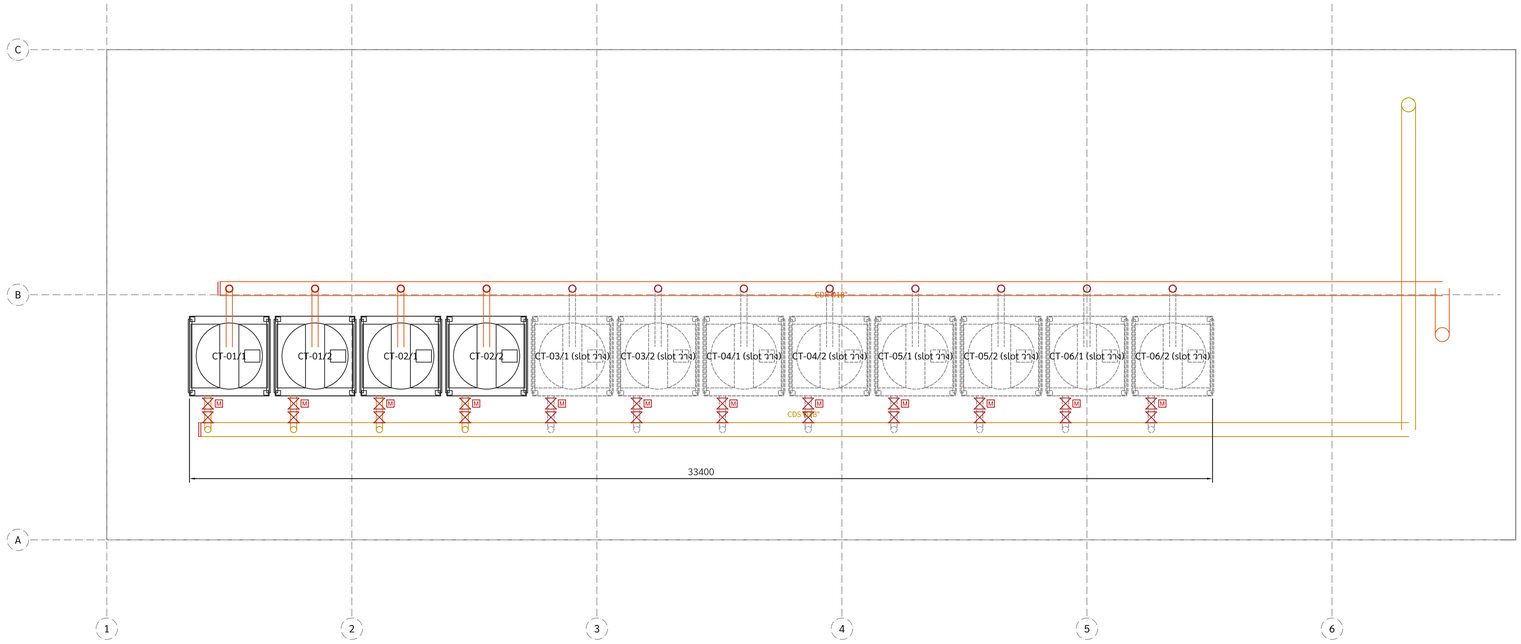

N

3 แปลนดาดฟ้า / ROOF PLAN (เฉพาะพื้นที่เหนือห้องเครื่อง)

มาตราส่วน 1:100

หมายเหตุ / NOTES

1. CT แต่ละชุด 2 cell ตั้งบนโครงเหล็ก (grillage) สูง 1.0 ม. จากพื้นดาดฟ้า
2. CT-01/02 = เครื่องเดิม V7.8 (MBFV เข้า/ออกแยก) · CT-03..06 = slot ขยาย (วาล์วชุดเดียว)
3. Header CDR จ่ายน้ำร้อนเข้าแต่ละ cell / header CDS รวมน้ำเย็นลง riser
4. OAU-01, EF, LSF, SEF อยู่บนดาดฟ้า (ดู M-104)

AETERLINK

AETERLINK (THAILAND) CO., LTD. · BMS / CPMS

PROJECT / โครงการ :
อาคารอ้างอิง 8 ชั้น (CPMS V7.9)
CPMS Reference Building V7.9
STATION :
ALT_CP_Ref_V7_9

OWNER / เจ้าของโครงการ :
[ระบุตามโครงการ]

BASIS / ที่มา :
Reference design for logic & graphics
Max. equipment 6 / type (register)
Site survey: NOT DONE (ต้องสำรวจ)

ENGINEERS / วิศวกรผู้ออกแบบ-ตรวจสอบ
วิศวกรเครื่องกล : .....
ใบอนุญาต ภก./สก. เลขที่ : .....
ลงนาม : ..... วันที่ : .....
วิศวกรไฟฟ้า : .....
ใบอนุญาต ภฟ./สฟ. เลขที่ : .....

REVISION / แก้ไข

A	08/10/2026	FOR REVIEW - generated from the V7.9 model

FOR REVIEW · ไม่ใช่แบบก่อสร้าง
NOT FOR CONSTRUCTION


DRAWING TITLE / ชื่อแบบ :
แปลนดาดฟ้า - หอระบายความร้อน 6 ชุด (12 cell)
ROOF PLAN - COOLING TOWERS

DRAWN : AETERLINK model generator
CHECKED : .....
APPROVED : .....
SCALE : 1:100 DATE : 08/10/2026

DRAWING NO. / เลขที่แบบ

M-103

หน่วยวัดเป็นมิลลิเมตร ระดับอ้างอิงพื้นชั้น 1 ±0.000

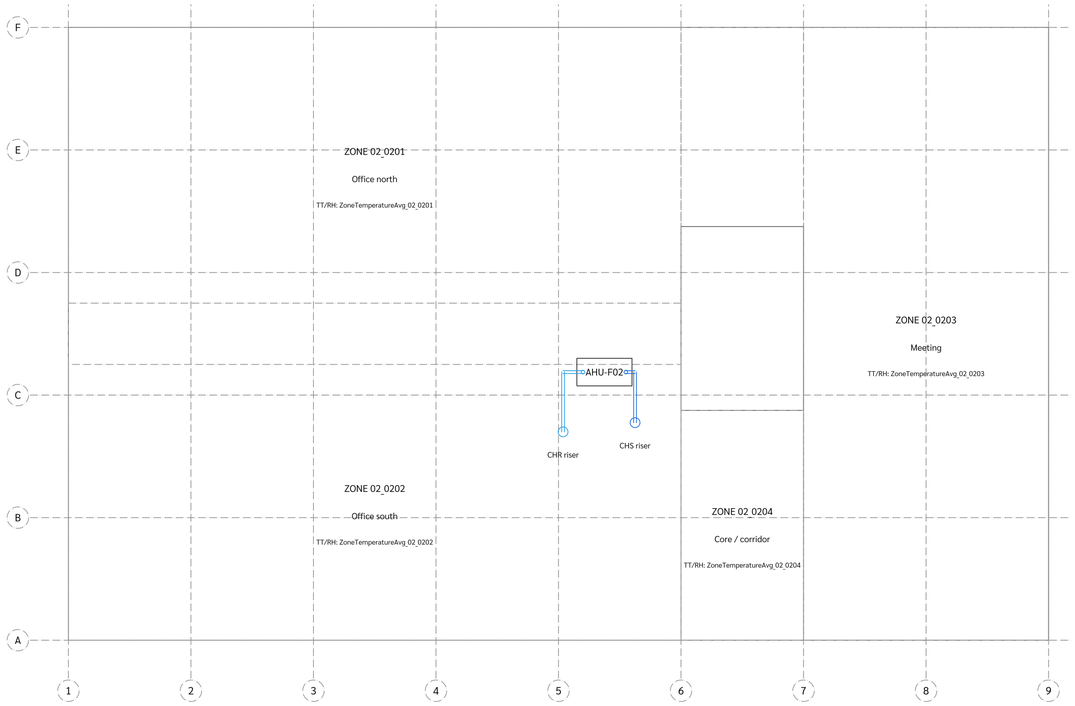

4 แปลนชั้นทั่วไป / TYPICAL FLOOR (ชั้น 2 แสดง, ชั้น 3-8 เหมือนกัน)

มาตราส่วน 1:200

หมายเหตุ / NOTES

1. AHU_Fnn ชั้นละ 1 ชุด คุม CHW valve ตามอุณหภูมิเฉลี่ย 4 zone (zone OOS ไม่นับ) + RH สูง = valve ชั้นต่ำ (dehum)
2. Zone code nn_nn01..04 = ZoneTemperatureAvg / ZoneHumidityAvg (AirPlug / Sense-T)
3. ท่อ CHW แยกจาก riser ใน shaft เข้า AHU ผ่าน MCV (AHU_Fnn_ValveCmd)
4. ระบบอื่นในอนาคต (fire alarm, sprinkler, lighting) เพิ่มใน register sheet Systems

N

AETERLINK

AETERLINK (THAILAND) CO., LTD. · BMS / CPMS

PROJECT / โครงการ :
อาคารอ้างอิง 8 ชั้น (CPMS V7.9)
CPMS Reference Building V7.9
STATION :
ALT_CP_Ref_V7_9

OWNER / เจ้าของโครงการ :
[ระบุตามโครงการ]

BASIS / ที่มา :
Reference design for logic & graphics
Max. equipment 6 / type (register)
Site survey: NOT DONE (ต้องสำรวจ)

ENGINEERS / วิศวกรผู้ออกแบบ-ตรวจสอบ
วิศวกรเครื่องกล : .....
ใบอนุญาต ภก./สก. เลขที่ : .....
ลงนาม : ..... วันที่ : .....
วิศวกรไฟฟ้า : .....
ใบอนุญาต ภฟ./สฟ. เลขที่ : .....

REVISION / แก้ไข

A	08/10/2026	FOR REVIEW - generated from the V7.9 model

FOR REVIEW · ไม่ใช่แบบก่อสร้าง

NOT FOR CONSTRUCTION


DRAWING TITLE / ชื่อแบบ :
แปลนชั้นทั่วไป 2-8 ระบบปรับอากาศ (AHU + zone)
TYPICAL FLOOR PLAN (FLOORS 2-8) - AIR SIDE

DRAWN : AETERLINK model generator
CHECKED : .....
APPROVED : .....
SCALE : 1:200 DATE : 08/10/2026

DRAWING NO. / เลขที่แบบ

M-104

หน่วยวัดเป็นมิลลิเมตร ระดับอ้างอิงพื้นชั้น 1 ±0.000

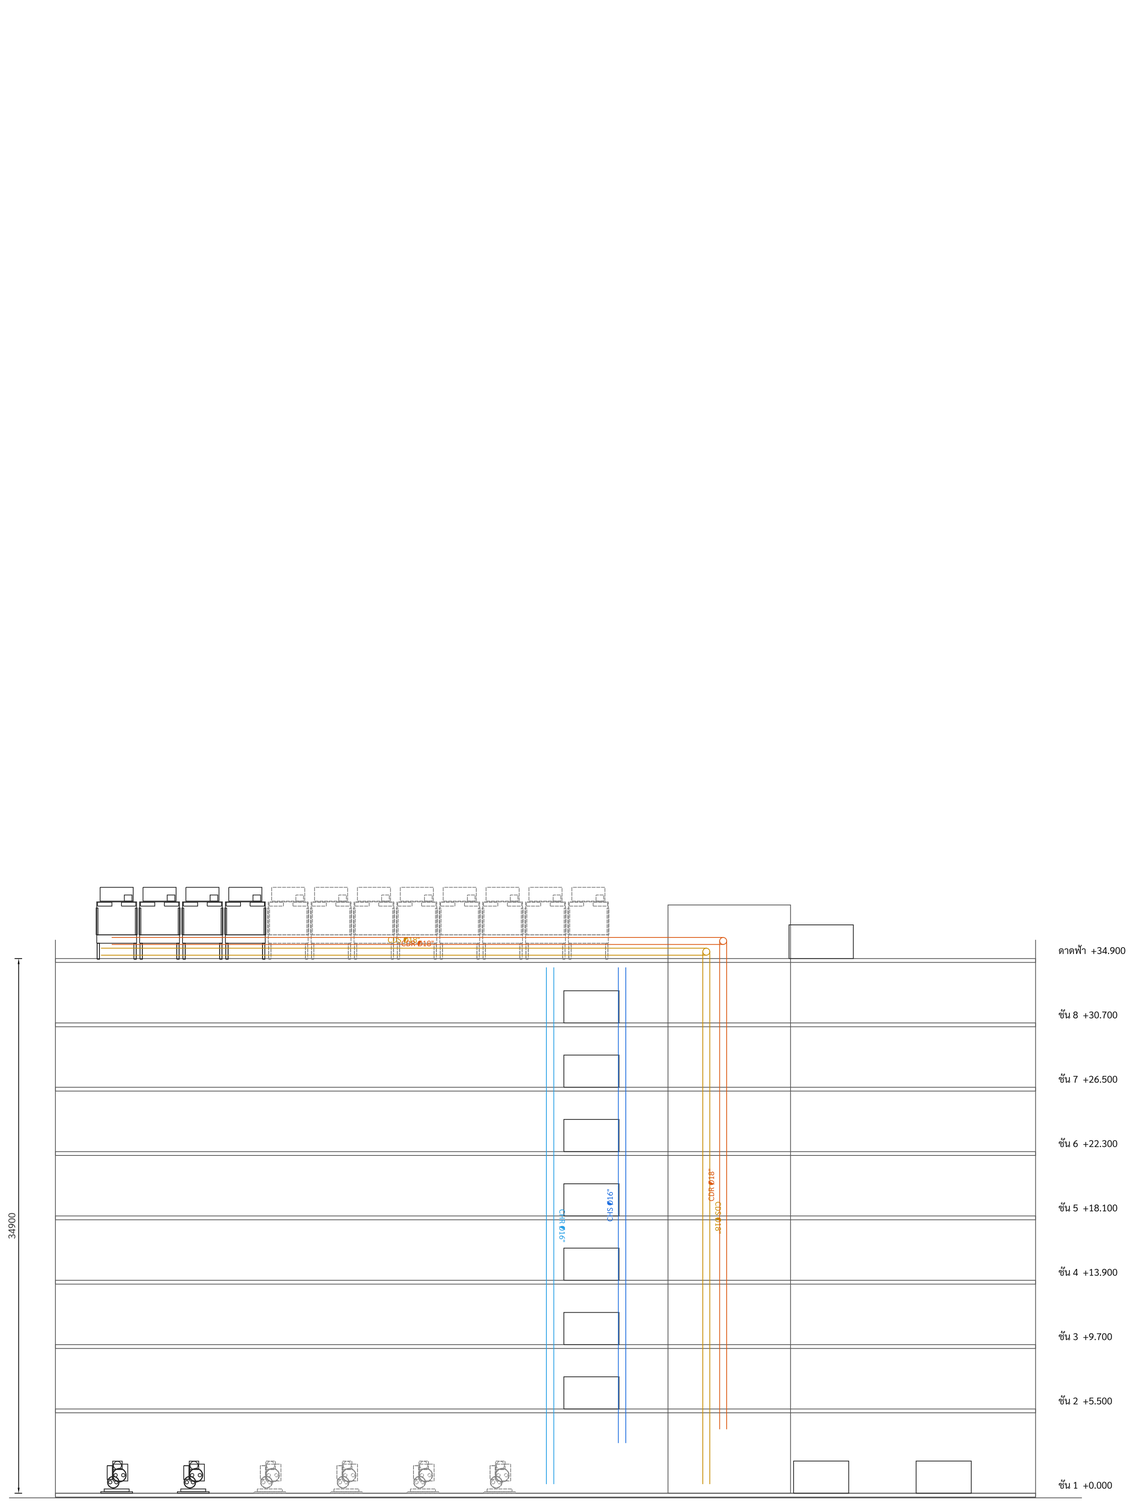

5 รูปตัดอาคาร / BUILDING SECTION (มองทิศเหนือ)
มาตราส่วน 1:200

AETERLINK
AETERLINK (THAILAND) CO., LTD. · BMS / CPMS

PROJECT / โครงการ :
อาคารอ้างอิง 8 ชั้น (CPMS V7.9)
CPMS Reference Building V7.9
STATION :
ALT_CP_Ref_V7_9

OWNER / เจ้าของโครงการ :
[ระบุตามโครงการ]

BASIS / ที่มา :
Reference design for logic & graphics
Max. equipment 6 / type (register)
Site survey: NOT DONE (ต้องสำรวจ)

ENGINEERS / วิศวกรผู้ออกแบบ-ตรวจสอบ
วิศวกรเครื่องกล : .....
ใบอนุญาต ภก./สก. เลขที่ : .....
ลงนาม : ..... วันที่ : .....
วิศวกรไฟฟ้า : .....
ใบอนุญาต ภฟ./สฟ. เลขที่ : .....

REVISION / แก้ไข

A	08/10/2026	FOR REVIEW - generated from the V7.9 model

FOR REVIEW · ไม่ใช่แบบก่อสร้าง
NOT FOR CONSTRUCTION


DRAWING TITLE / ชื่อแบบ :
รูปตัดอาคาร (ห้องเครื่องชั้น 1 - riser - cooling tower ดาดฟ้า)
BUILDING SECTION

DRAWN : AETERLINK model generator
CHECKED : .....
APPROVED : .....
SCALE : 1:200 DATE : 08/10/2026

DRAWING NO. / เลขที่แบบ

M-201

หน่วยวัดเป็นมิลลิเมตร ระดับอ้างอิงพื้นชั้น 1 ±0.000

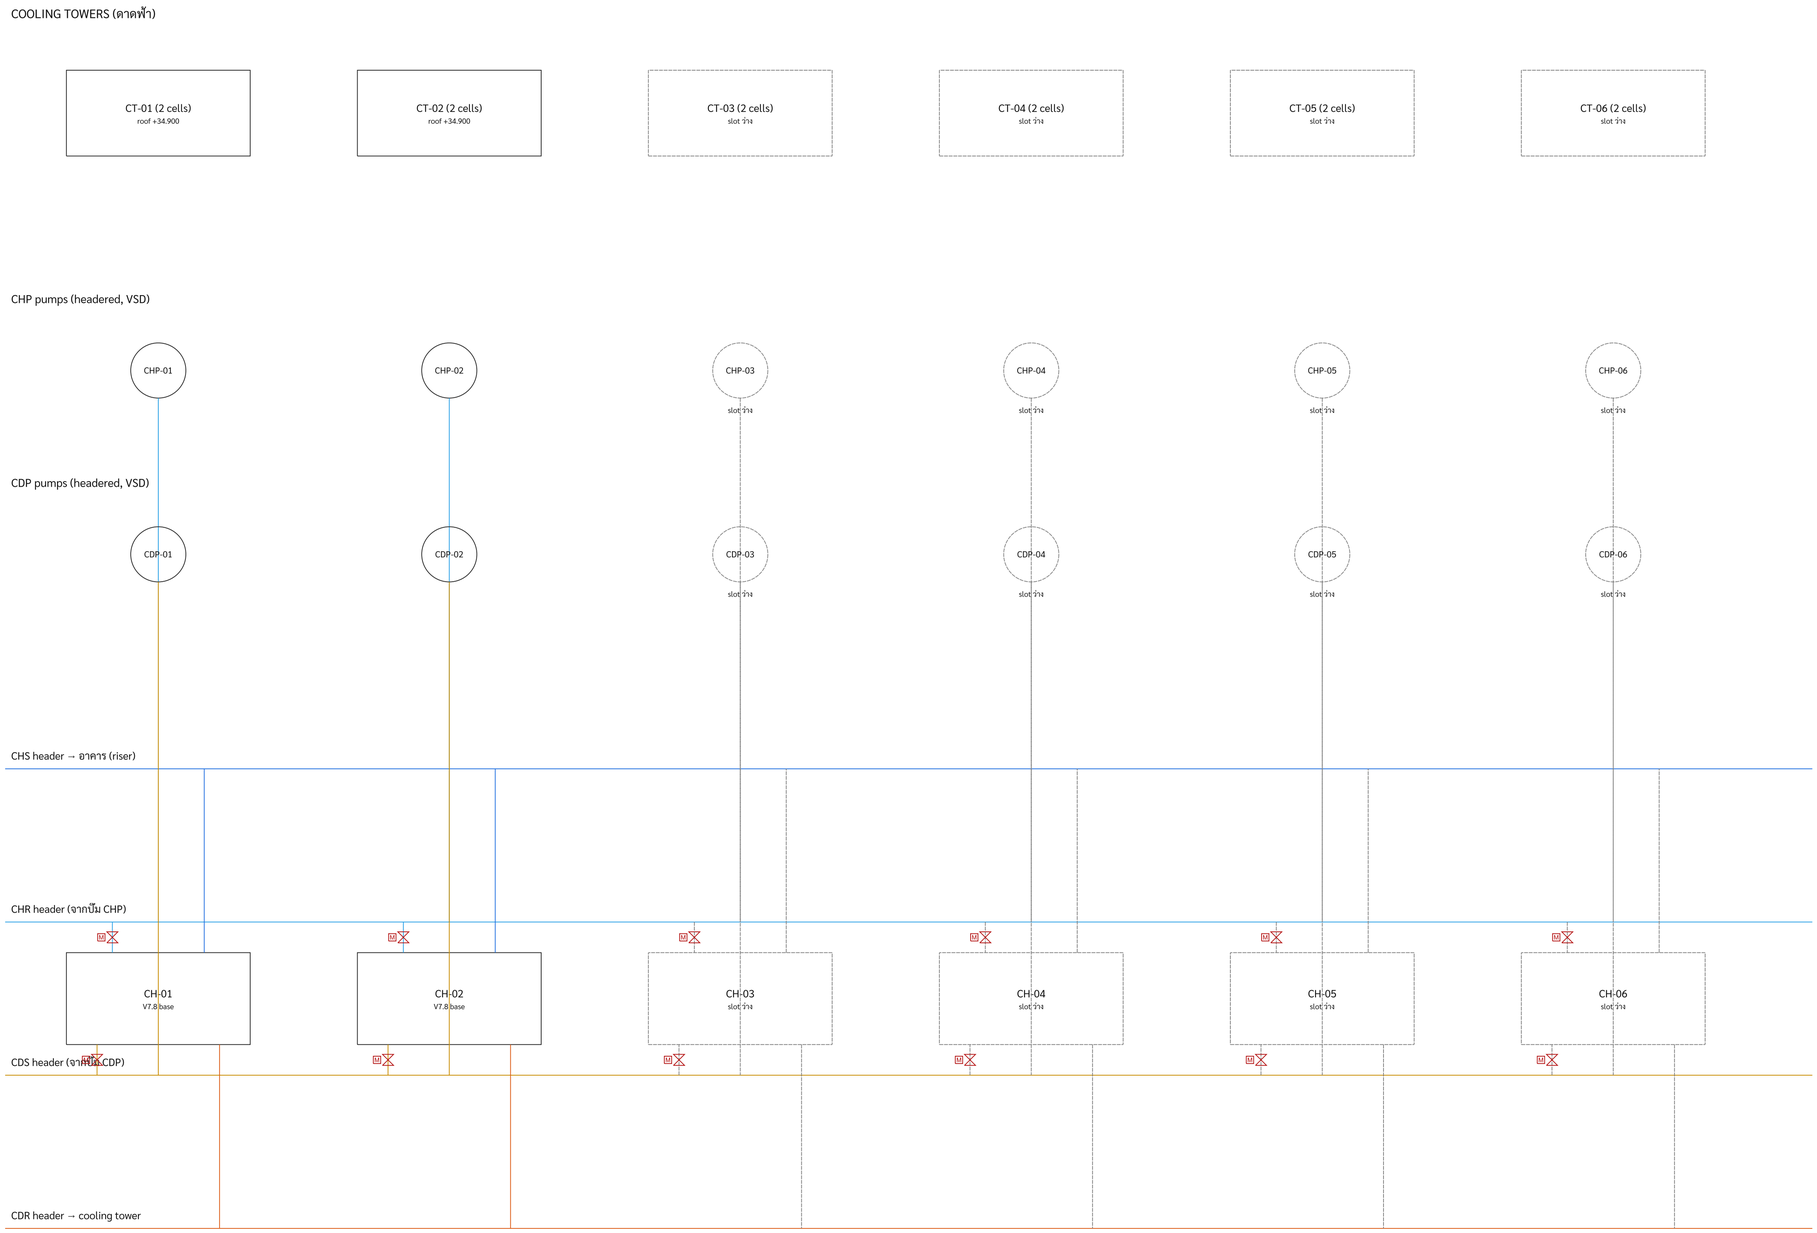

หมายเหตุ / NOTES

1. ทุกชนิดมี 6 slot: 01-02 = เครื่องเดิม V7.8 (logic เดิม), 03-06 = slot ขยาย (Expansion/<slot> ใน station)
2. เส้นประ = ยังไม่ติดตั้ง · เปิดใช้งาน: ตั้ง <slot>_Installed = true หรือแก้ register แล้วสร้างใหม่
3. ลำดับเดิน slot 03 → 06 ข้ามเครื่องที่ไม่พร้อม (fault / maintenance / start fail) อัตโนมัติ
4. จำนวน CHP / CDP / CT ที่เดิน = จำนวน chiller ที่ต้องการน้ำ (รวม post-run) ลบด้วยเครื่องเดิมที่พร้อม

AETERLINK

AETERLINK (THAILAND) CO., LTD. · BMS / CPMS

PROJECT / โครงการ :
อาคารอ้างอิง 8 ชั้น (CPMS V7.9)
CPMS Reference Building V7.9
STATION :
ALT_CP_Ref_V7_9

OWNER / เจ้าของโครงการ :
[ระบุตามโครงการ]

BASIS / ที่มา :
Reference design for logic & graphics
Max. equipment 6 / type (register)
Site survey: NOT DONE (ต้องสำรวจ)

ENGINEERS / วิศวกรผู้ออกแบบ-ตรวจสอบ
วิศวกรเครื่องกล : .....
ใบอนุญาต ภก./สก. เลขที่ : .....
ลงนาม : ..... วันที่ : .....
วิศวกรไฟฟ้า : .....
ใบอนุญาต ภฟ./สฟ. เลขที่ : .....

REVISION / แก้ไข

A	08/10/2026	FOR REVIEW - generated from the V7.9 model

FOR REVIEW · ไม่ใช่แบบก่อสร้าง
NOT FOR CONSTRUCTION

DRAWING TITLE / ชื่อแบบ :
แผนผังระบบท่อน้ำเย็น / น้ำระบายความร้อน (6 slot ต่อชนิด)
CHW / CDW SCHEMATIC - 6 SLOTS PER TYPE

DRAWN : AETERLINK model generator
CHECKED : .....
APPROVED : .....
SCALE : NTS DATE : 08/10/2026

DRAWING NO. / เลขที่แบบ

M-501

หน่วยวัดเป็นมิลลิเมตร ระดับอ้างอิงพื้นชั้น 1 ±0.000



AETERLINK

AETERLINK (THAILAND) CO., LTD. · BMS / CPMS

PROJECT / โครงการ :
อาคารอ้างอิง 8 ชั้น (CPMS V7.9)
CPMS Reference Building V7.9
STATION :
ALT_CP_Ref_V7_9

OWNER / เจ้าของโครงการ :
[ระบุตามโครงการ]

BASIS / ที่มา :
Reference design for logic & graphics
Max. equipment 6 / type (register)
Site survey: NOT DONE (ต้องสำรวจ)

ENGINEERS / วิศวกรผู้ออกแบบ-ตรวจสอบ
วิศวกรเครื่องกล : .....
ใบอนุญาต ภก./สก. เลขที่ : .....
ลงนาม : ..... วันที่ : .....
วิศวกรไฟฟ้า : .....
ใบอนุญาต ภฟ./สฟ. เลขที่ : .....

REVISION / แก้ไข

A	08/10/2026	FOR REVIEW - generated from the V7.9 model

FOR REVIEW · ไม่ใช่แบบก่อสร้าง
NOT FOR CONSTRUCTION

DRAWING TITLE / ชื่อแบบ :
แผนผัง riser น้ำเย็นไป AHU ทุกชั้น
CHW RISER DIAGRAM

DRAWN : AETERLINK model generator
CHECKED : .....
APPROVED : .....
SCALE : NTS DATE : 08/10/2026

DRAWING NO. / เลขที่แบบ

M-502

หน่วยวัดเป็นมิลลิเมตร ระดับอ้างอิงพื้นชั้น 1 ±0.000

TAG	TYPE	DESCRIPTION / MODEL	CAPACITY / RATING	LOCATION	QTY	BMS POINT
CH-01	CHILLER	Water-cooled screw / centrifugal (reference)	334 TR · 0.614 kW/TR	ชั้น 1	ติดตั้ง	CH01
CH-02	CHILLER	Water-cooled screw / centrifugal (reference)	334 TR · 0.614 kW/TR	ชั้น 1	ติดตั้ง	CH02
CH-03	CHILLER	Water-cooled screw / centrifugal (reference)	334 TR · 0.614 kW/TR	ชั้น 1	slot ว่า	CH03
CH-04	CHILLER	Water-cooled screw / centrifugal (reference)	334 TR · 0.614 kW/TR	ชั้น 1	slot ว่า	CH04
CH-05	CHILLER	Water-cooled screw / centrifugal (reference)	334 TR · 0.614 kW/TR	ชั้น 1	slot ว่า	CH05
CH-06	CHILLER	Water-cooled screw / centrifugal (reference)	334 TR · 0.614 kW/TR	ชั้น 1	slot ว่า	CH06
CHP-01	PUMP	Chilled water pump (primary-variable, headered)	800 USgpm · 80 ft · 22 kW, 380/3/50	ชั้น 1	ติดตั้ง	CHP01
CHP-02	PUMP	Chilled water pump (primary-variable, headered)	800 USgpm · 80 ft · 22 kW, 380/3/50	ชั้น 1	ติดตั้ง	CHP02
CHP-03	PUMP	Chilled water pump (primary-variable, headered)	800 USgpm · 80 ft · 22 kW, 380/3/50	ชั้น 1	slot ว่า	CHP03
CHP-04	PUMP	Chilled water pump (primary-variable, headered)	800 USgpm · 80 ft · 22 kW, 380/3/50	ชั้น 1	slot ว่า	CHP04
CHP-05	PUMP	Chilled water pump (primary-variable, headered)	800 USgpm · 80 ft · 22 kW, 380/3/50	ชั้น 1	slot ว่า	CHP05
CHP-06	PUMP	Chilled water pump (primary-variable, headered)	800 USgpm · 80 ft · 22 kW, 380/3/50	ชั้น 1	slot ว่า	CHP06
CDP-01	PUMP	Condenser water pump (headered)	1,000 USgpm · 80 ft · 30 kW, 380/3/50	ชั้น 1	ติดตั้ง	CDP01
CDP-02	PUMP	Condenser water pump (headered)	1,000 USgpm · 80 ft · 30 kW, 380/3/50	ชั้น 1	ติดตั้ง	CDP02
CDP-03	PUMP	Condenser water pump (headered)	1,000 USgpm · 80 ft · 30 kW, 380/3/50	ชั้น 1	slot ว่า	CDP03
CDP-04	PUMP	Condenser water pump (headered)	1,000 USgpm · 80 ft · 30 kW, 380/3/50	ชั้น 1	slot ว่า	CDP04
CDP-05	PUMP	Condenser water pump (headered)	1,000 USgpm · 80 ft · 30 kW, 380/3/50	ชั้น 1	slot ว่า	CDP05
CDP-06	PUMP	Condenser water pump (headered)	1,000 USgpm · 80 ft · 30 kW, 380/3/50	ชั้น 1	slot ว่า	CDP06
CT-01/1	CT	Crossflow, induced draft (FRP)	420 TR per tower · 5.5 kW VSD	ROOF	ติดตั้ง	CT01_01
CT-01/2	CT	Crossflow, induced draft (FRP)	420 TR per tower · 5.5 kW VSD	ROOF	ติดตั้ง	CT01_02
CT-02/1	CT	Crossflow, induced draft (FRP)	420 TR per tower · 5.5 kW VSD	ROOF	ติดตั้ง	CT02_01
CT-02/2	CT	Crossflow, induced draft (FRP)	420 TR per tower · 5.5 kW VSD	ROOF	ติดตั้ง	CT02_02
CT-03/1	CT	Crossflow, induced draft (FRP)	420 TR per tower · 5.5 kW VSD	ROOF	slot ว่า	CT03
CT-03/2	CT	Crossflow, induced draft (FRP)	420 TR per tower · 5.5 kW VSD	ROOF	slot ว่า	CT03
CT-04/1	CT	Crossflow, induced draft (FRP)	420 TR per tower · 5.5 kW VSD	ROOF	slot ว่า	CT04
CT-04/2	CT	Crossflow, induced draft (FRP)	420 TR per tower · 5.5 kW VSD	ROOF	slot ว่า	CT04
CT-05/1	CT	Crossflow, induced draft (FRP)	420 TR per tower · 5.5 kW VSD	ROOF	slot ว่า	CT05
CT-05/2	CT	Crossflow, induced draft (FRP)	420 TR per tower · 5.5 kW VSD	ROOF	slot ว่า	CT05
CT-06/1	CT	Crossflow, induced draft (FRP)	420 TR per tower · 5.5 kW VSD	ROOF	slot ว่า	CT06
CT-06/2	CT	Crossflow, induced draft (FRP)	420 TR per tower · 5.5 kW VSD	ROOF	slot ว่า	CT06
ET-01	EXPTANK	Expansion tank	1,000 L	ชั้น 1	ติดตั้ง	-
DPB-01	BYPASS	CHW minimum-flow bypass		ชั้น 1	ติดตั้ง	Byp
CP-01	PANEL	CPMS control panel (Niagara JACE / Supervisor)		ชั้น 1	ติดตั้ง	Plant
AHU-01	AHU	Air handling unit, CHW coil, VSD fan	12,000 CFM	ชั้น 1	ติดตั้ง	AHU01
AHU-02	AHU	Air handling unit, CHW coil, VSD fan	12,000 CFM	ชั้น 1	ติดตั้ง	AHU02
OAU-01	AHU	Outdoor air unit (dew point control)		ROOF	ติดตั้ง	OAU01
FCU-01	FCU	Fan coil unit, 3-speed fan, on/off valve		ชั้น 1	ติดตั้ง	FCU01
FCU-02	FCU	Fan coil unit, 3-speed fan, on/off valve		ชั้น 1	ติดตั้ง	FCU02
FCU-03	FCU	Fan coil unit, 3-speed fan, on/off valve		ชั้น 1	ติดตั้ง	FCU03
FCU-04	FCU	Fan coil unit, 3-speed fan, on/off valve		ชั้น 1	ติดตั้ง	FCU04
AHU-F02	AHU	Air handling unit, CHW coil, VSD fan	12,000 CFM	ชั้น 2	ติดตั้ง	AHU_F02
AHU-F03	AHU	Air handling unit, CHW coil, VSD fan	12,000 CFM	ชั้น 3	ติดตั้ง	AHU_F03
AHU-F04	AHU	Air handling unit, CHW coil, VSD fan	12,000 CFM	ชั้น 4	ติดตั้ง	AHU_F04
AHU-F05	AHU	Air handling unit, CHW coil, VSD fan	12,000 CFM	ชั้น 5	ติดตั้ง	AHU_F05
AHU-F06	AHU	Air handling unit, CHW coil, VSD fan	12,000 CFM	ชั้น 6	ติดตั้ง	AHU_F06
AHU-F07	AHU	Air handling unit, CHW coil, VSD fan	12,000 CFM	ชั้น 7	ติดตั้ง	AHU_F07
AHU-F08	AHU	Air handling unit, CHW coil, VSD fan	12,000 CFM	ชั้น 8	ติดตั้ง	AHU_F08
EF-01	FAN	Fan		ROOF	ติดตั้ง	EF01
EF-02	FAN	Fan		ROOF	ติดตั้ง	EF02
EF-03	FAN	Fan		ชั้น 1	ติดตั้ง	EF03
CPEF-01	FAN	Fan		ROOF	ติดตั้ง	CPEF01
LSF-01	FAN	Fan		ROOF	ติดตั้ง	LSF01
SEF-01	FAN	Fan		ROOF	ติดตั้ง	SEF01

AETERLINK
AETERLINK (THAILAND) CO., LTD. · BMS / CPMS

PROJECT / โครงการ :
อาคารอ้างอิง 8 ชั้น (CPMS V7.9)
CPMS Reference Building V7.9
STATION :
ALT_CP_Ref_V7_9

OWNER / เจ้าของโครงการ :
[ระบุตามโครงการ]

BASIS / ที่มา :
Reference design for logic & graphics
Max. equipment 6 / type (register)
Site survey: NOT DONE (ต้องสำรวจ)

ENGINEERS / วิศวกรผู้ออกแบบ-ตรวจสอบ
วิศวกรเครื่องกล : .....
ใบอนุญาต ภก./สก. เลขที่ : .....
ลงนาม : ..... วันที่ : .....
วิศวกรไฟฟ้า : .....
ใบอนุญาต ภฟ./สฟ. เลขที่ : .....

REVISION / แก้ไข
A 08/10/2026 FOR REVIEW - generated from the V7.9 model

FOR REVIEW · ไม่ใช่แบบก่อสร้าง
NOT FOR CONSTRUCTION

DRAWING TITLE / ชื่อแบบ :
ตารางรายการอุปกรณ์
EQUIPMENT SCHEDULE

DRAWN : AETERLINK model generator
CHECKED : .....
APPROVED : .....
SCALE : NTS DATE : 08/10/2026

DRAWING NO. / เลขที่แบบ

M-601

หน่วยวัดเป็นมิลลิเมตร ระดับอ้างอิงพื้นชั้น 1 ±0.000